

DIVISÃO DE ACESSIBILIDADE

PROJETO N°: 10034

COMPRADOR/ CONTRATANTE:

Obra/ Edificação:

Endereço:

CARACTERÍSTICAS DO EQUIPAMENTO:

- Modelo:	KIT COMPONENTES EH01 6 PASS
- Capacidade:	450Kg OU 6 PASSAGEIROS
- Base:	1,00 x 1,25m
- Velocidade:	36m/min
- N° de Paradas:	03 PARADAS
- Enclausuramento	ALVENARIA PELO CLIENTE
- Desnível total:	+8,00m
- Última altura:	3,20m
- Poço:	-0,90m
- Acionamento:	Hidráulico
- Entradas:	UNILATERAIS (360°)
- Posição da Torre:	ESQUERDA
- Porta de Cabina:	AUTOMÁTICA LATERAL ESQUERDA
- Porta de Pavimento:	AUTOMÁTICA LATERAL ESQUERDA - TIPO "B"
- Identificação de Pavimento:	0 ; 1
- Classificação:	USO RESTRITO
- Acabamento Interno Cabina:	CONFORME PROPOSTA COMERCIAL
- Bloco Hidráulico:	EV100
- Acessórios:	CONFORME PROPOSTA COMERCIAL

ÍNDICE

Serviços de Responsabilidade do Cliente	02
Planta Baixa	03
Vistas	04
Cortes	05

RESPONSABILIDADE DO CLIENTE:

1 – AS VIGAS DE CONCRETO OU METÁLICAS AONDE SERÁ FIXADA A ESTRUTURA DO ELEVADOR DEVERÃO SER FORNECIDAS PELO CLIENTE. ESTE DEVERÁ CONSULTAR O ENGENHEIRO CALCULISTA PARA DIMENSIONAR AS VIGAS DE CONCRETO, PARA QUE SUPOTEM AS CARGAS ESTÁTICAS E DINÂMICAS (VER DET. CARGAS)

2 – ABAIXO DO POÇO O CLIENTE DEVE EXECUTAR FUNDAÇÃO ADEQUADA PARA RESISTIR AS CARGAS ESTÁTICAS E DINÂMICAS DA ESTRUTURA DO ELEVADOR INDICADO NO PROJETO.

3 – A CONSTRUÇÃO DA CAIXA DE CORRIDA É POR CONTA DO CLIENTE. COMO OS ESPAÇOS DENTRO DA MESMA SÃO REDUZIDOS, É ESSENCIAL QUE SEJA OBSERVADO O NIVELAMENTO DO PISO, ESQUADROS ENTRE AS PAREDES, PRUMADAS E SOLEIRAS DE PORTA, NENHUMA FERRAGEM DO ENCLAUSURAMENTO DEVE PROJETAR-SE PARA O INTERIOR DA CAIXA DE CORRIDA.

4 – O ENCLAUSURAMENTO DA CAIXA DE CORRIDA DEVE SER SOLIDAMENTE FECHADO EM TODA A SUA EXTENSÃO, SEM GRADES OU ABERTURAS , SENDO PERMITIDAS APENAS PORTAS DE PAVIMENTO E PORTA DE MANUTENÇÃO.

5 – A CAIXA DE CORRIDA DEVE SER DE USO EXCLUSIVO DO ELEVADOR, NÃO SENDO PERMITIDO SEU USO COMO DEPÓSITO OU INSTALAÇÃO DE EQUIPAMENTOS ALHEIOS.

6 – O CLIENTE DEVE FORNECER QUADRO DE DISTRIBUIÇÃO EXCLUSIVO PARA O ATENDIMENTO DO QUADRO DE COMANDO DO ELEVADOR. AS INFORMAÇÕES NECESSÁRIAS PARA O QUADRO DE COMANDO DO ELEVADOR. AS INFORMAÇÕES NECESSÁRIAS PARA O QUADRO FORNECER TENSÃO INDICADA NO DIAGRAMA.

7 – O CLIENTE DEVE FORNECER ELETROCALHA COM TAMPA NO TRECHO ENTRE O QUADRO DE COMANDO E UNIDADE HIDRÁULICA E DOS MESMO ATÉ OS FUROS PARA PASSAGEM DOS CABOS E MANGUEIRA HIDRÁULICA.

8 – ILUMINAÇÃO (ELETRODUTOS, ELETROCALHAS, LUMINÁRIAS, INTERRUPTORES E TOMADA) DENTRO DA CAIXA DE CORRIDA SÃO POR CONTA DO CLIENTE, DEVENDO SER ORIGINADOS DO QUADRO DE DISTRIBUIÇÃO DO CLIENTE.

9 – A CAIXA DE CORRIDA DEVE ESTAR IMUNE A INFILTRAÇÃO E UMIDADE.

10 – EXECUTAR ACABAMENTO ENTRE PORTA E PAREDE PÓS INSTALAÇÃO CASO SEJA NECESSÁRIO.


11 – A UNIDADE HIDRÁULICA E QUADRO DE COMANDO DEVEM ESTAR PROTEGIDOS DE CHUVA E SOL.

12 – AS PAREDES LATERAIS DA CAIXA DEVEM POSSUIR ACABAMENTO LISO E DE COR CLARA ADMITINDO-SE O ACABAMENTO SEM REBOCO DESDE QUE SEJA DE TEXTURA EQUIPÁVEL À DO CONCRETO À VISTA. CONFORME ITEM 5.3 NBR NM 267: 2001.

Alteração	Descrição	Data	Responsável
00	EMISSÃO INICIAL		
	Edifício:	Projeto N°:	Escala:
			INDEFINIDA
	Especificação Técnica		
Índice: Roteiro - Serviços de Responsabilidade do Cliente		Folha Número:	02

ATENÇÃO

- Todas as cotas estão expressas em mm.
- Desenho meramente Ilustrativo e sem escala.

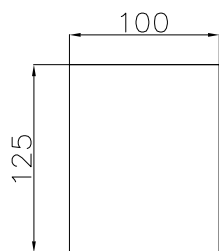


Medidas Apenas para
Referência (Orçamento)
Espessura Máxima 30mm
(Granito + Massa)



MEDIDAS INTERNAS DA CABINA PARA
COLOCAÇÃO DO PISO (PELO CLIENTE)

HL03 RESIDENCIAL

225 Kg (3 Passag.)- capacidade nominal

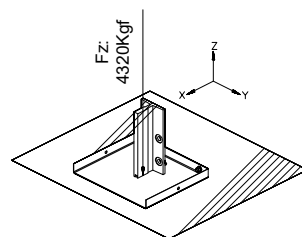

REAÇÕES DAS GUIAS
NO FUNDO DO POÇO

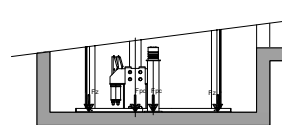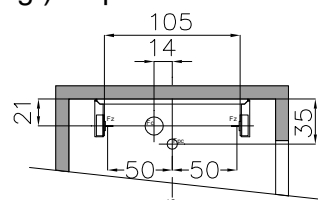

Fz	Reação sob a guia	4320 Kg
Fc	Reação sob o cilindro	3330 Kg
Fpc	Reação sob o paracheque	7400 Kg

ELÉTRICA DENTRO DA CAIXA DE CORRIDA

LUMINÁRIA (Em todos os pavimentos)


INTERRUPTOR EM PARALELO

TOMADA 220


ELETROCAHA EM "C" (10x5cm) PERFURADA EM TODA A
EXTENSÃO DA CAIXA DE CORRIDA

PORTAS DE PAV. TIPO "B"


- COM CAIXILHO
- TRILHO E CAIXILHO DENTRO DA CAIXA DE CORRIDA
- SEM RECORTE NA SOLEIRA
- ENTRADAS UNILATERAIS

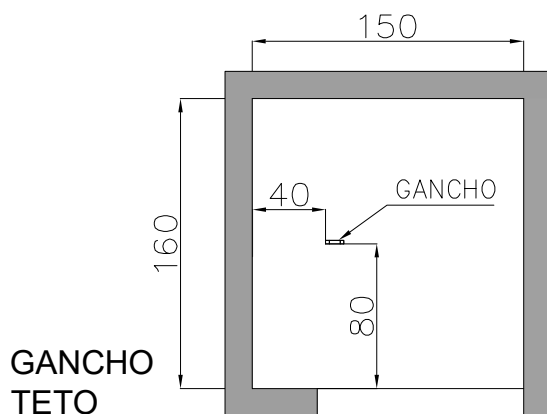

GANCHO
TETO

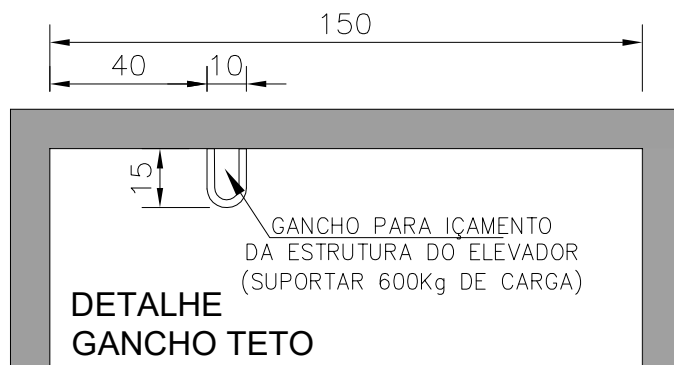


DETALHE
GANCHO TETO

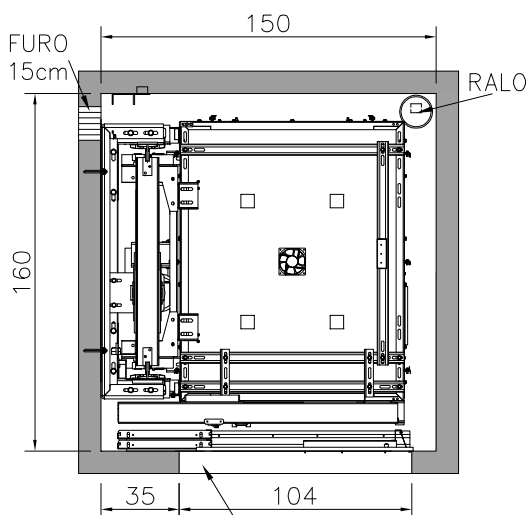

TÉRREO

VÃO ABERTO NA LARGURA
PARA FIXAÇÃO DA PORTA

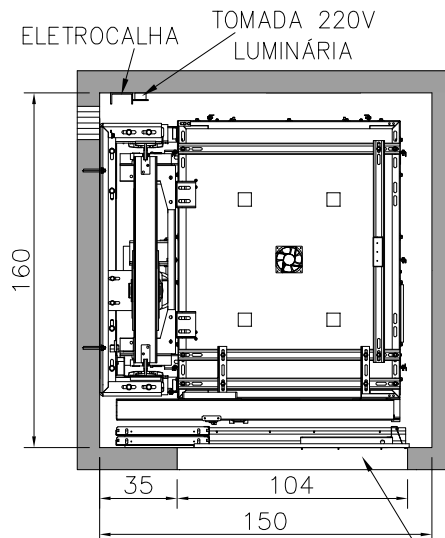

SUPERIORES


VÃO ABERTO NA LARGURA
PARA FIXAÇÃO DA PORTA

Alteração	Descrição	Data	Responsável
00	EMIÇÃO INICIAL		


	Edifício:	Projeto N°:	Escala:
	Especificação Técnica		INDEFINIDA
Índice: Planta Baixa		Folha Número:	03

ATENÇÃO

- Todas as cotas estão expressas em mm. Desenho meramente Ilustrativo e sem escala.

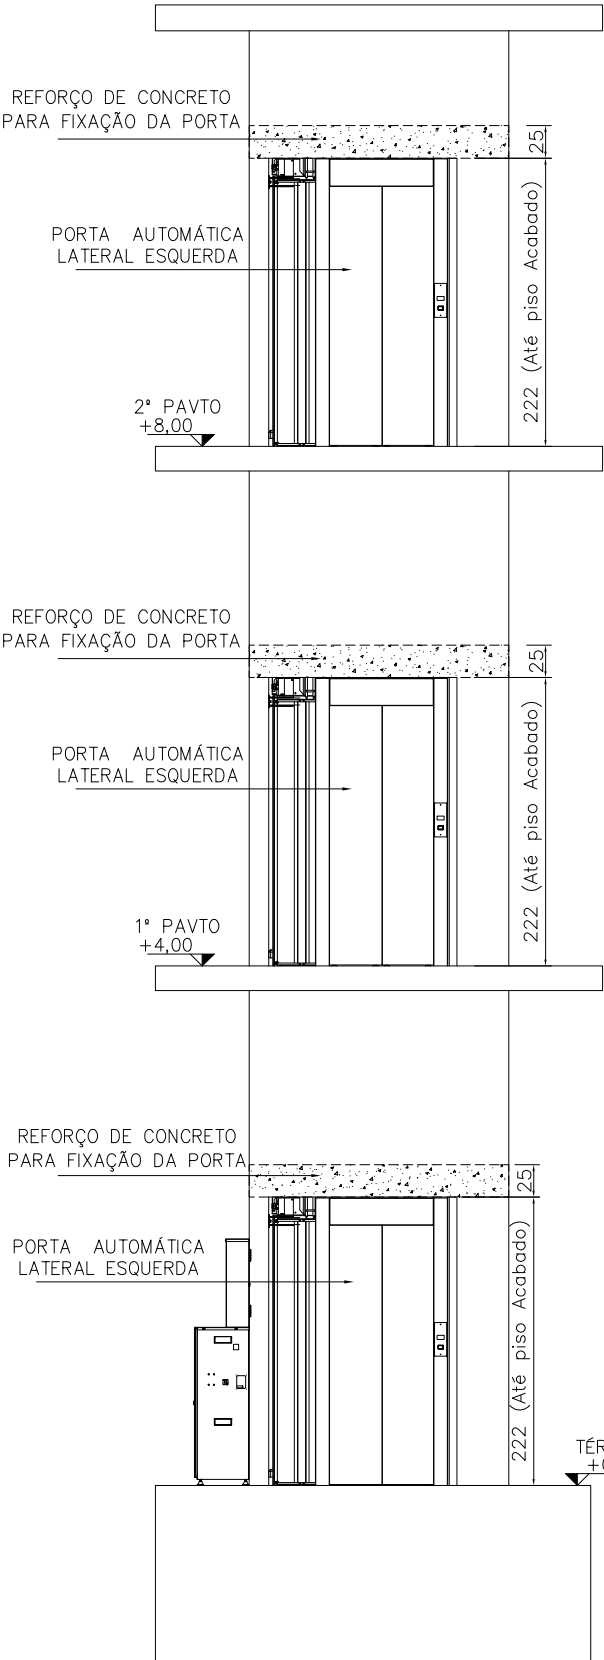

VISTA FRONTAL

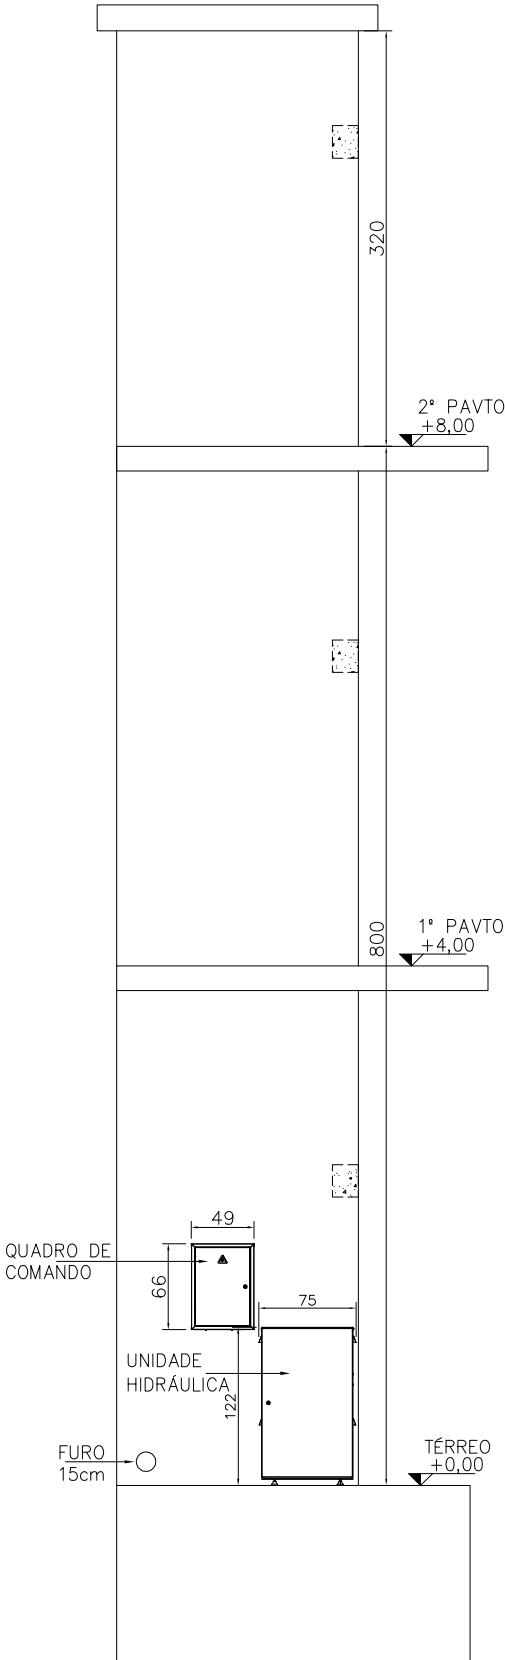


VISTA LATERAL ESQUERDA

Alteração	Descrição	Data	Responsável
00	EMIÇÃO INICIAL		

	Edifício:	Projeto N°:	Escala: INDEFINIDA
	Especificação Técnica		Folha Número: 04

ATENÇÃO

- Todas as cotas estão expressas em mm. Desenho meramente Ilustrativo e sem escala.

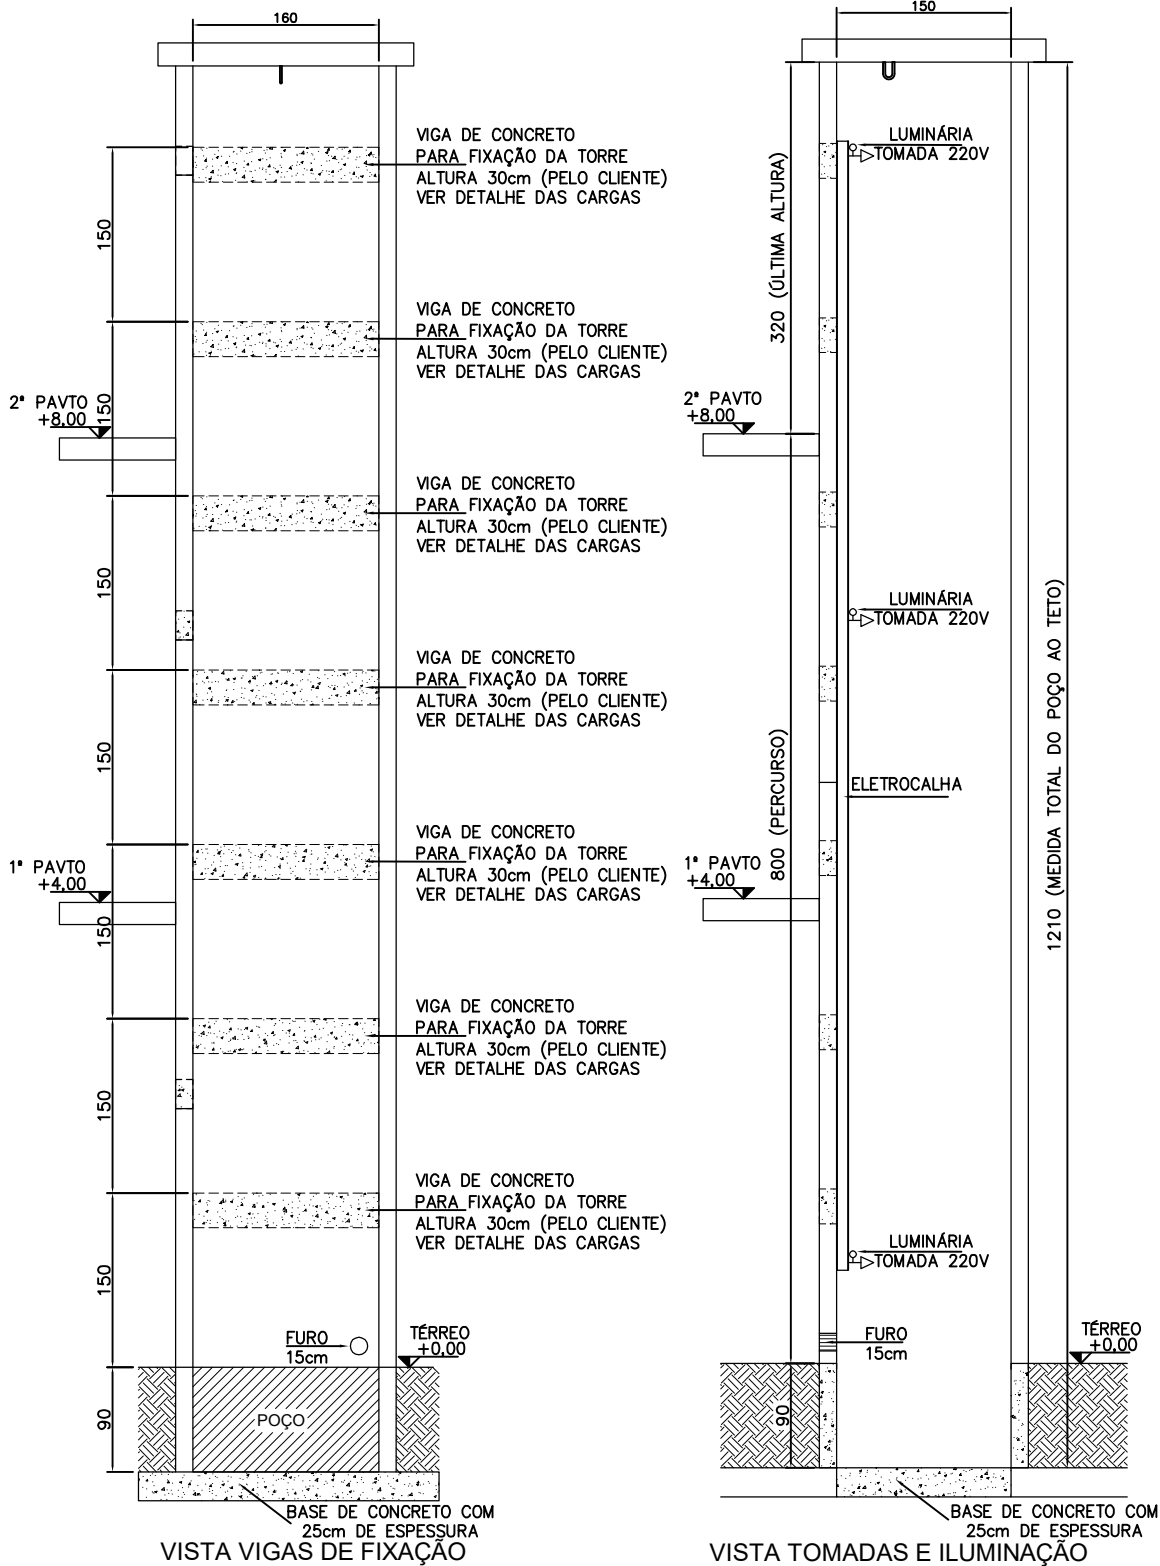

O FORNECIMENTO E INSTALAÇÃO DOS ELETRODUTOS, LUMINÁRIAS, TOMADAS E INTERRUPTORES SÃO DE RESPONSABILIDADE DO CLIENTE E DEVERÃO SER ALIMENTADOS PELO QUADRO DE DISTRIBUIÇÃO DO CLIENTE.

OS ACABAMENTOS LATERAIS DE PORTA SER EXECUTADOS PELO CLIENTE APÓS A INSTALAÇÃO DO ELEVADOR

Alteração	Descrição	Data	Responsável
00	EMISSÃO INICIAL		

	Edifício:	Projeto N°:	Escala: INDEFINIDA
	Especificação Técnica		Folha Número: 05